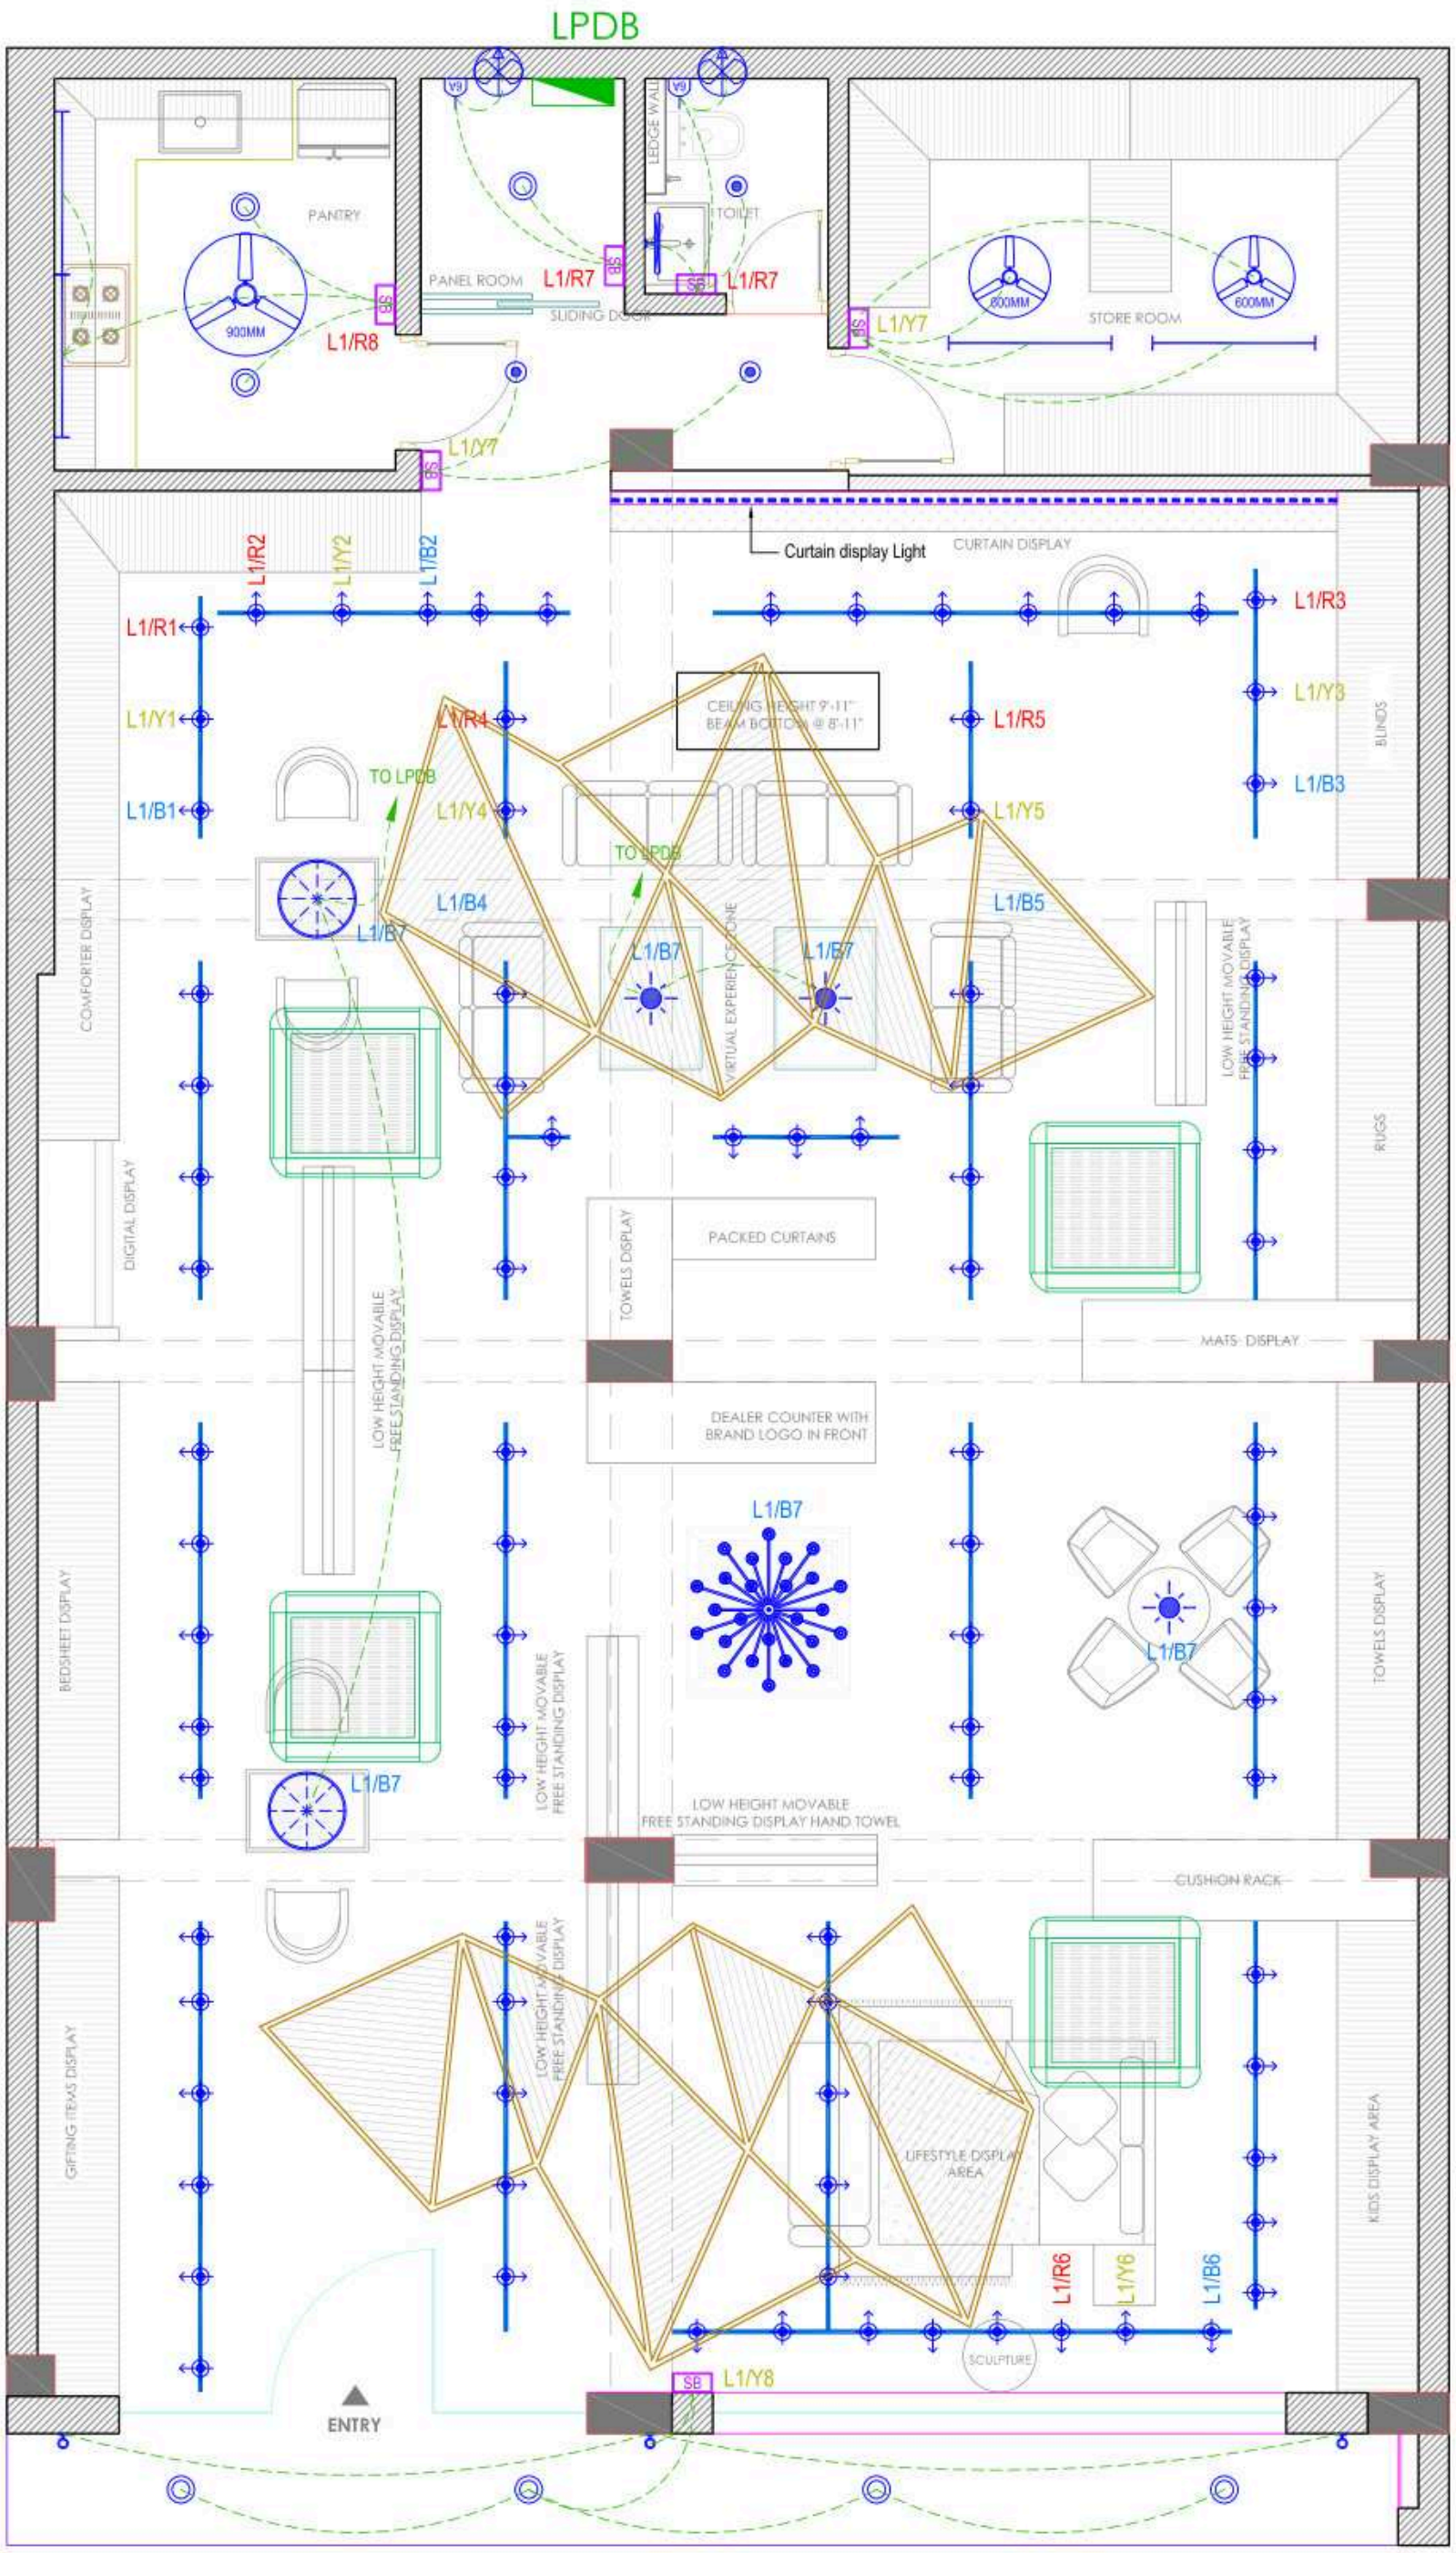


ELECTRICAL LEGEND:-

SYMBOL	DESCRIPTION
	18W CEILING RECESSED LED LIGHT
	10W LED DOWN LIGHT
	CHANDELIER LIGHT
	9W PENDANT LIGHT
	18W TRACK LIGHT (18W EACH)
	20W LED TUBE LIGHT
	18W LED UP DOWN LIGHTER
	CONDUIT JUNCTION BOX
	EXHAUST FAN
	6A POWER POINT FOR EXHAUST FAN CONTROL SB
	SWITCH BOARD
	DISTRIBUTION BOARD (DB)
	MIRROR LIGHT
	LINEAR LED STRIP
	25MM CONDUIT FOR POWER
	25MM CONDUIT FOR FLOOR LIGHTING
	25MM CONDUIT FOR CEILING LIGHTING

ARCHITECTS :	NOTES :	PROJECT TITLE :-	DRAWING TITLE :-	DRAWING ISSUED:	DATE	18.07.2024	REVISIONS	NO.	DATE	REMARKS	DWG. NO -
STUDIO PIRALI 135 D, Mathura Road New Delhi Contact No:- 9560834775 studiopirali@gmail.com.com	1. THIS DRAWING IS THE PROPERTY OF **STUDIO PIRALI** & SHALL NOT BE USED IN ANY WAY WITHOUT THEIR WRITTEN PERMISSION. 2. ALL DIMENSION ARE IN MM. UNLESS OTHERWISE MENTIONED. 3. WRITTEN DIMENSION ARE TO BE FOLLOWED. DRAWING NOT TO BE SCALED. 4. STRUCTURAL DWG TO BE REFEREED ALONG WITH ARCHITECTURAL DWG. 5. CONTRACTOR SHOULD VERIFY THE DRAWINGS IN FIELD BEFORE COMMENCEMENT OF THE WORK 6. IN CASE OF ANY DISCREPANCY CONTACT **STUDIO PIRALI** PRIOR TO EXECUTION.	HOME EXPERIA BEGUSARAI, BIHAR	CEILING LIGHTING LAYOUT	☑ FOR APPROVAL ☐ GOOD FOR CONSTRUCTION ☐ FOR INFORMATION ONLY	DEALT BY CHECKED BY SCALE	Jai Prakash Dipendra N.T.S		01 02 03			N W E S