



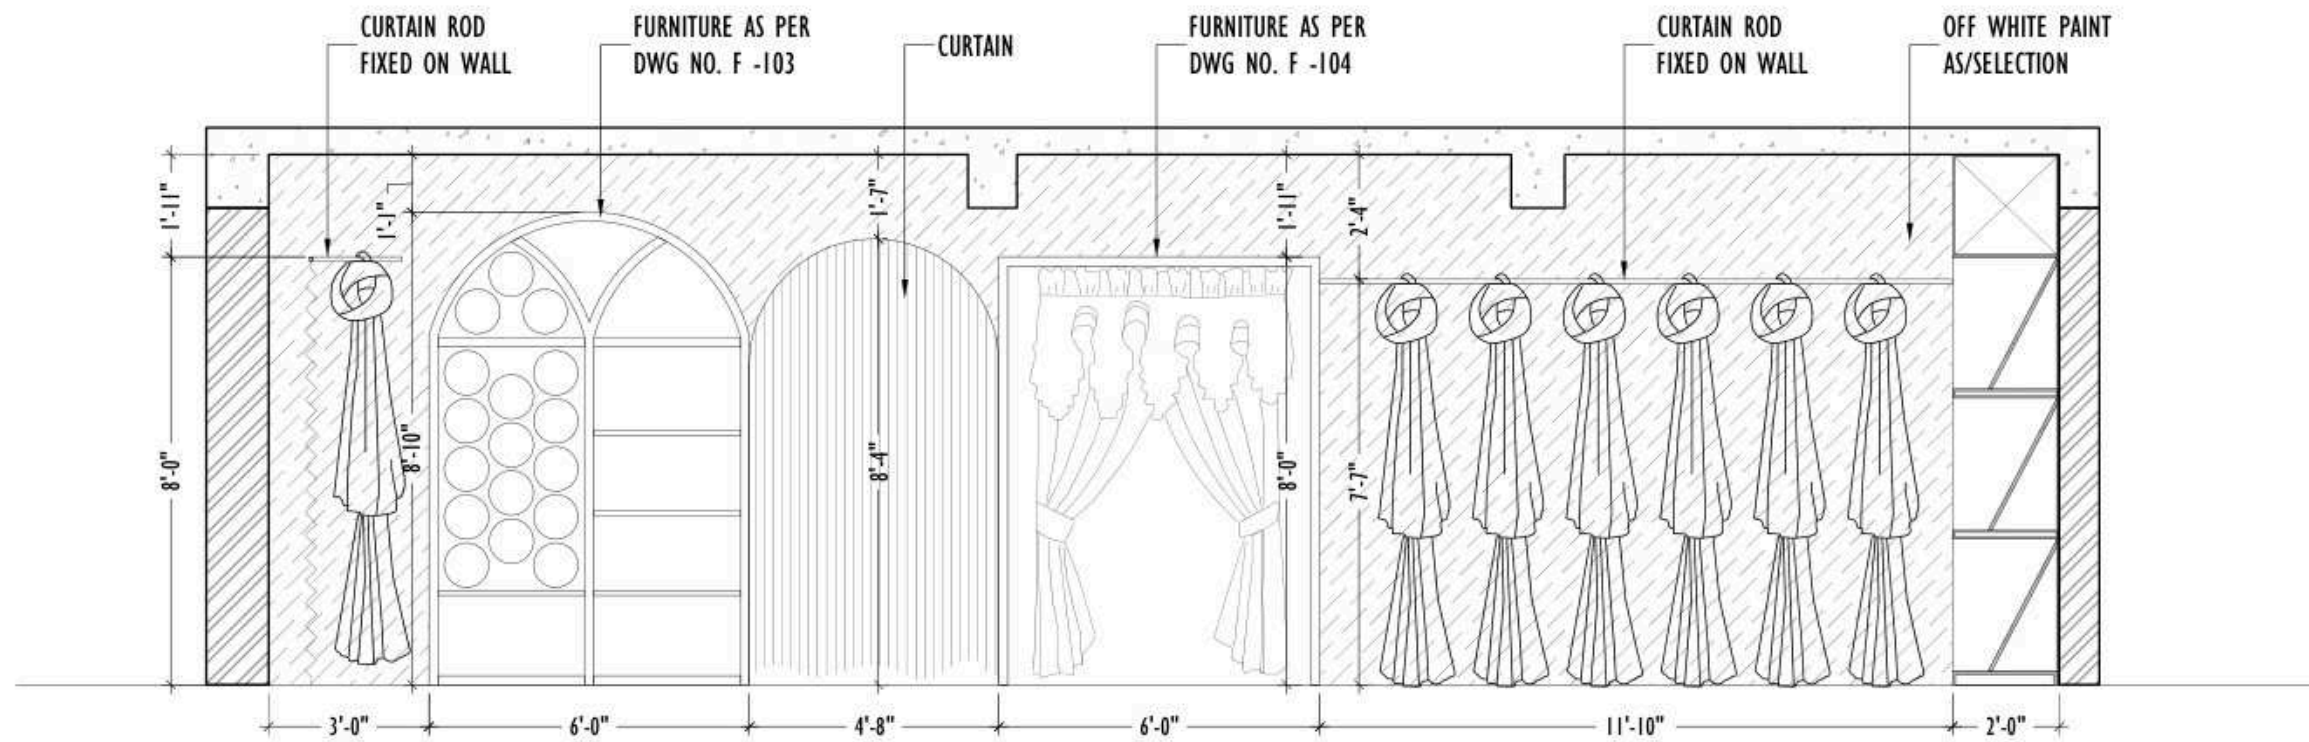

ELEVATION-2

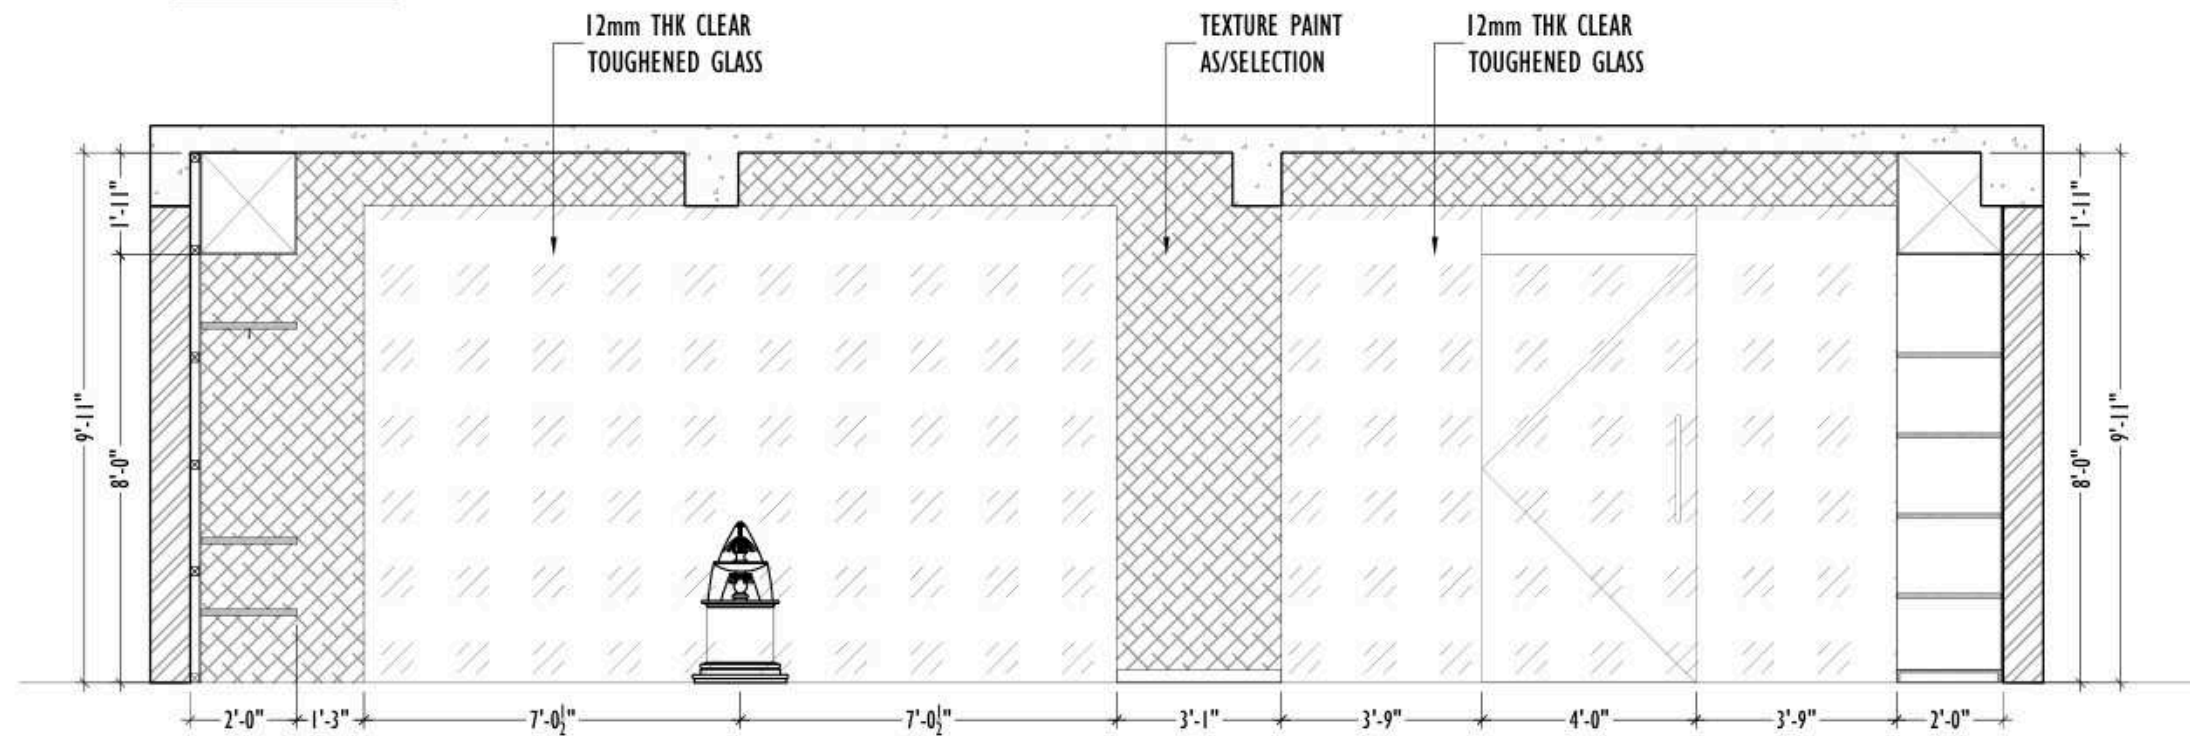

ELEVATION-4

ARCHITECTS :



STUDIO PIRALI
135 D, Ground floor, Opposite
Guwahati Club
Guwahati 781003
Contact No:- 9560834775
studiopirali@gmail.com

NOTES :

1. THIS DRAWING IS THE PROPERTY OF **STUDIO PIRALI** & SHALL NOT BE USED IN ANY WAY WITHOUT THEIR WRITTEN PERMISSION.
2. ALL DIMENSION ARE IN MM. UNLESS OTHERWISE MENTIONED.
3. WRITTEN DIMENSION ARE TO BE FOLLOWED. DRAWING NOT TO BE SCALED.
4. STRUCTURAL DWG. TO BE REFERRED ALONG WITH ARCHITECTURAL DWG.
5. CONTRACTOR SHOULD VERIFY THE DRAWINGS IN FIELD BEFORE COMMENCEMENT OF THE WORK.
6. IN CASE OF ANY DISCREPANCY CONTACT **STUDIO PIRALI** PRIOR TO EXECUTION.

PROJECT TITLE

HOME EXPERIA
Begusarai, Bihar

DRAWING TITLE :-

ELEVATION-2 & 4

DRAWING ISSUED:



FOR APPROVAL



GOOD FOR CONSTRUCTION



FOR INFORMATION ONLY

DATE

27.07.2024

DEALT BY

CHECKED BY

SCALE

Dipankar

N.T.S

REVISIONS

NO.	DATE	REMARKS	DWG. NO - F-108
01			
02			
03			