



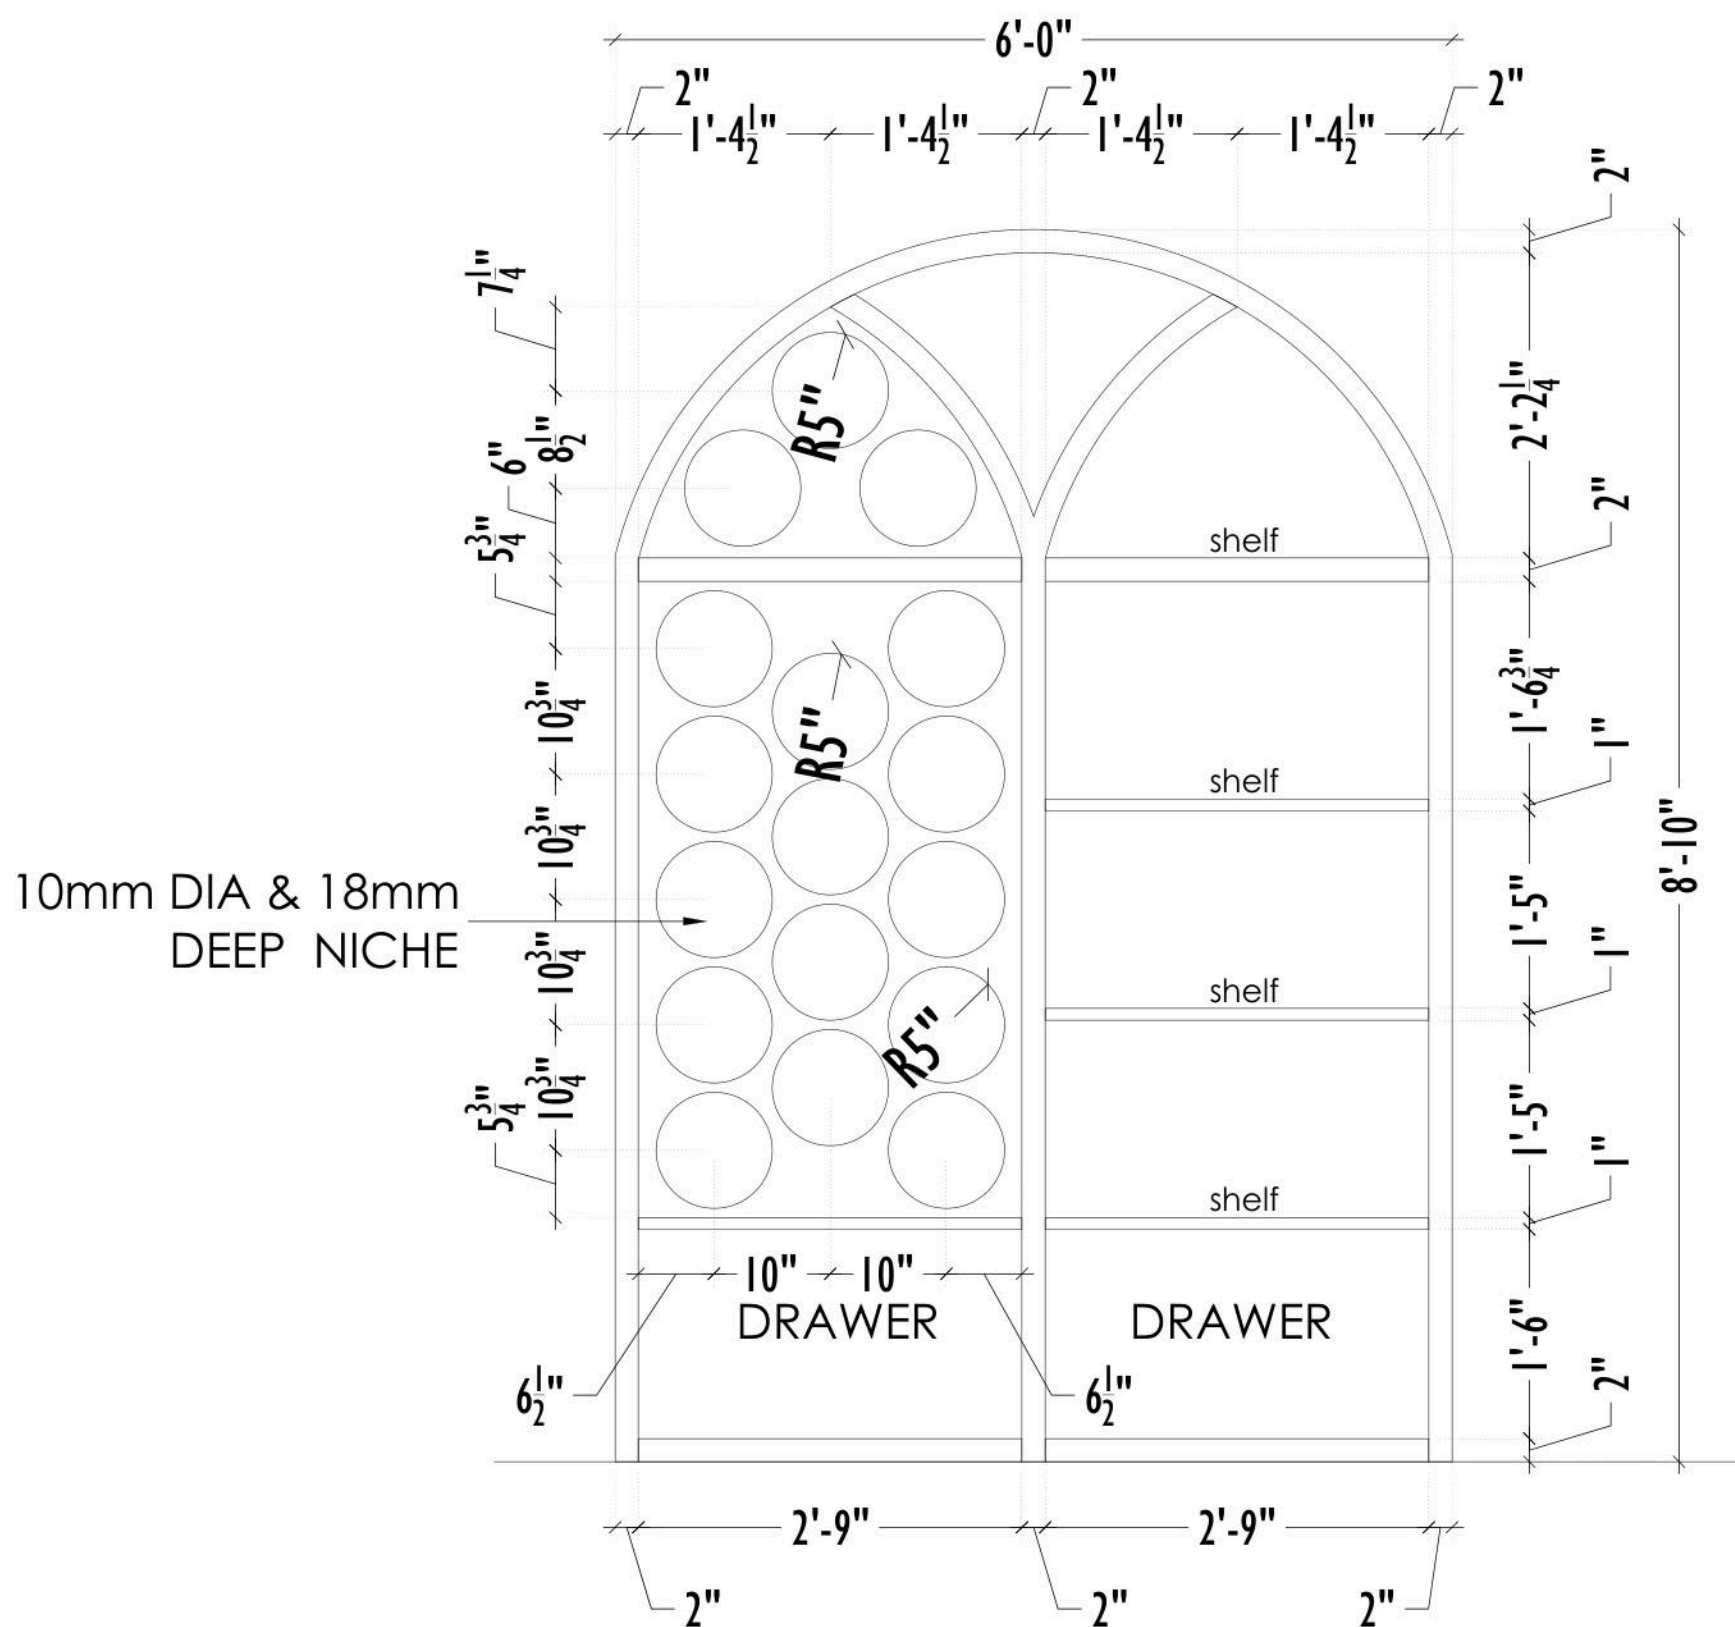

ELEVATION

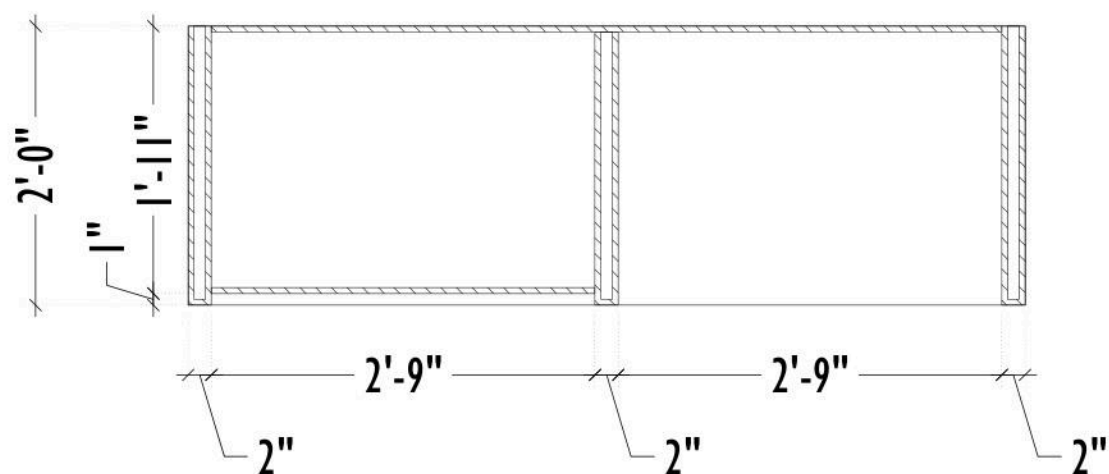

PLAN

ARCHITECTS :	NOTES :	PROJECT TITLE	DRAWING TITLE :-	DRAWING ISSUED:	DATE	27.07.2024	NO.	DATE	REMARKS	DWG. NO -F-103
 STUDIO PIRALI 135 D, Ground floor, Opposite Guwahati Club Guwahati 781003 Contact No:- 9560834775 studiopirali@gmail.com	1. THIS DRAWING IS THE PROPERTY OF STUDIO PIRALI & SHALL NOT BE USED IN ANY WAY WITHOUT THEIR WRITTEN PERMISSION. 2. ALL DIMENSION ARE IN MM, UNLESS OTHERWISE MENTIONED. 3. WRITTEN DIMENSION ARE TO BE FOLLOWED. DRAWING NOT TO BE SCALED. 4. STRUCTURAL DWG TO BE REFERRED ALONG WITH ARCHITECTURAL DWG. 5. CONTRACTOR SHOULD VERIFY THE DRAWINGS IN FIELD BEFORE COMMENCEMENT OF THE WORK. 6. IN CASE OF ANY DISCREPANCY CONTACT STUDIO PIRALI PRIOR TO EXECUTION.	HOME EXPERIA Begusarai, Bihar	FURNITURE DETAIL-3	☒ FOR APPROVAL	DEALT BY					
				☐ GOOD FOR CONSTRUCTION	CHECKED BY	<i>Dipankar</i>				
				☐ FOR INFORMATION ONLY	SCALE	N.T.S				