




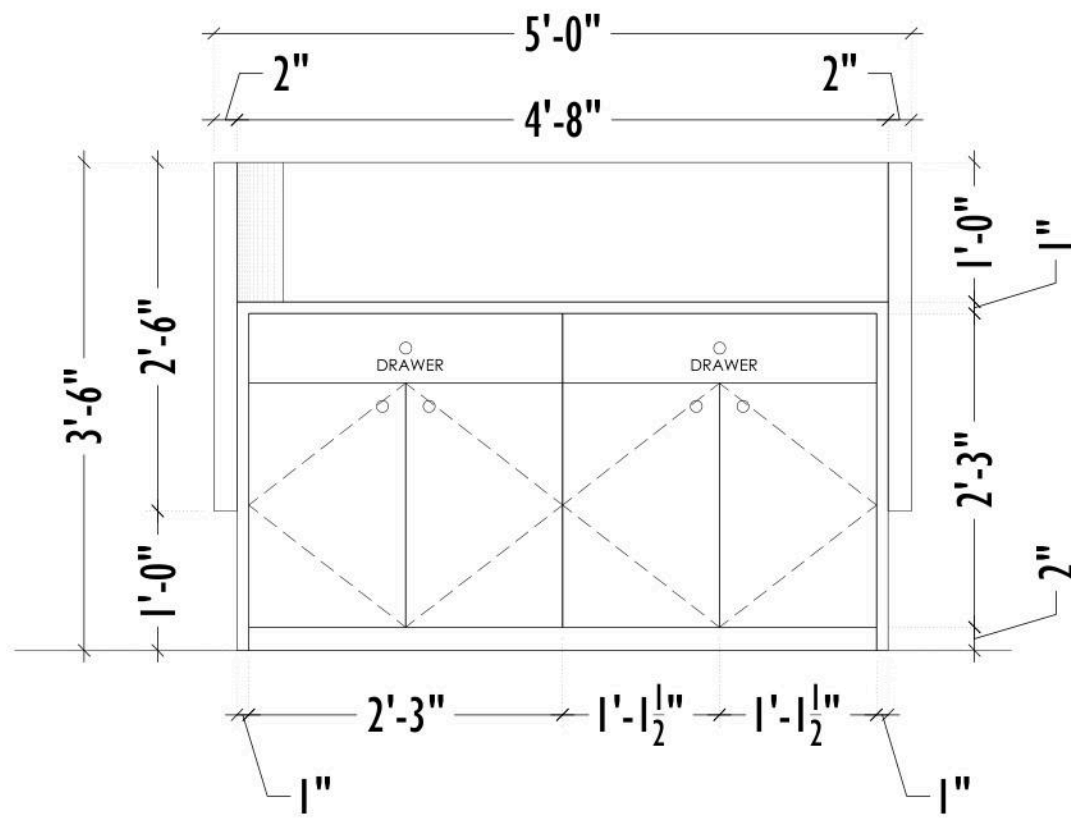


REAR ELEVATION

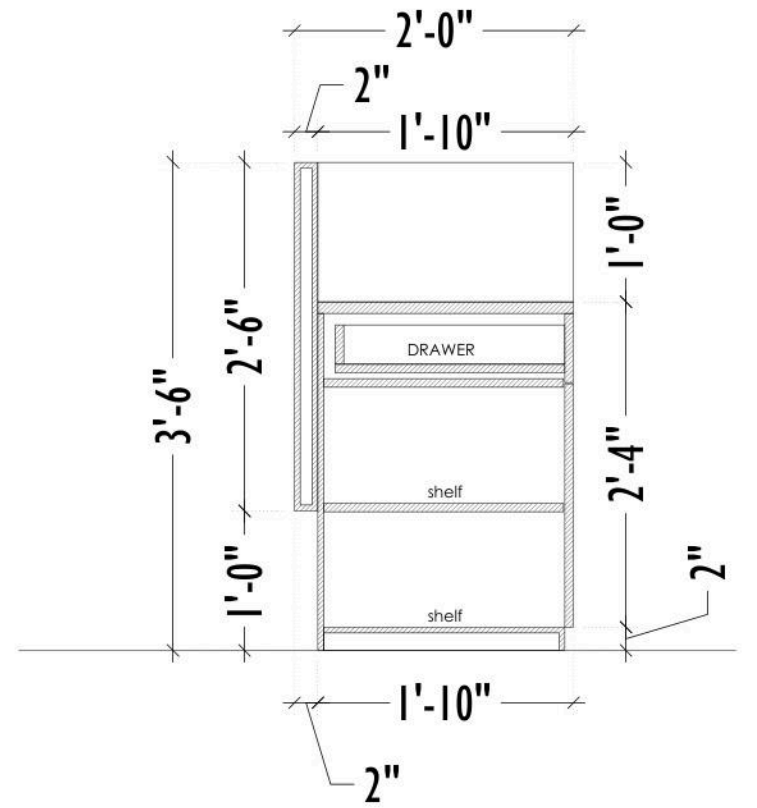


SECTION A-A'

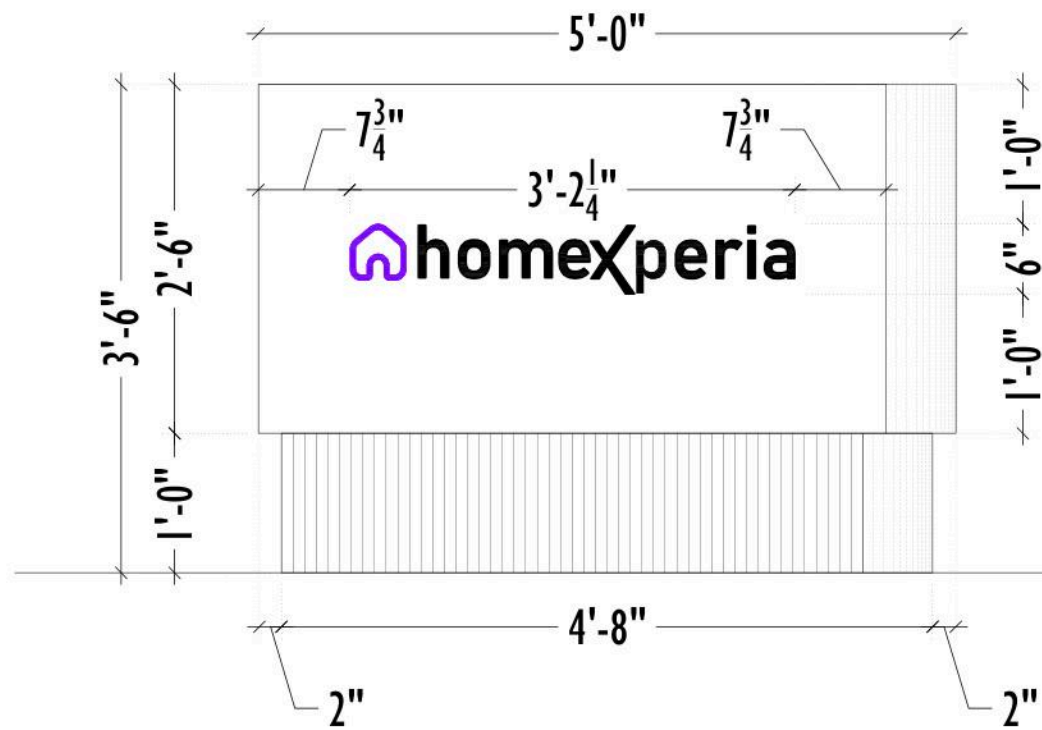


FRONT ELEVATION

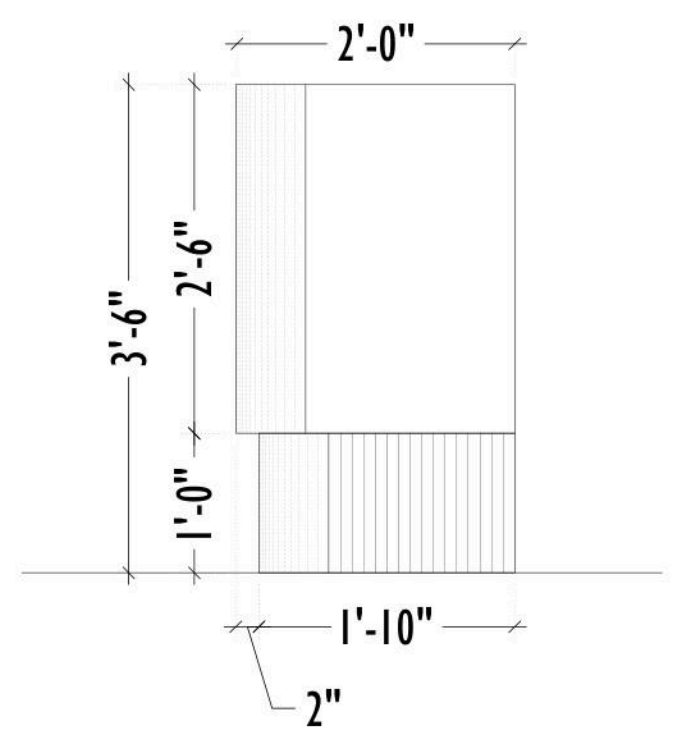

SIDE ELEVATION

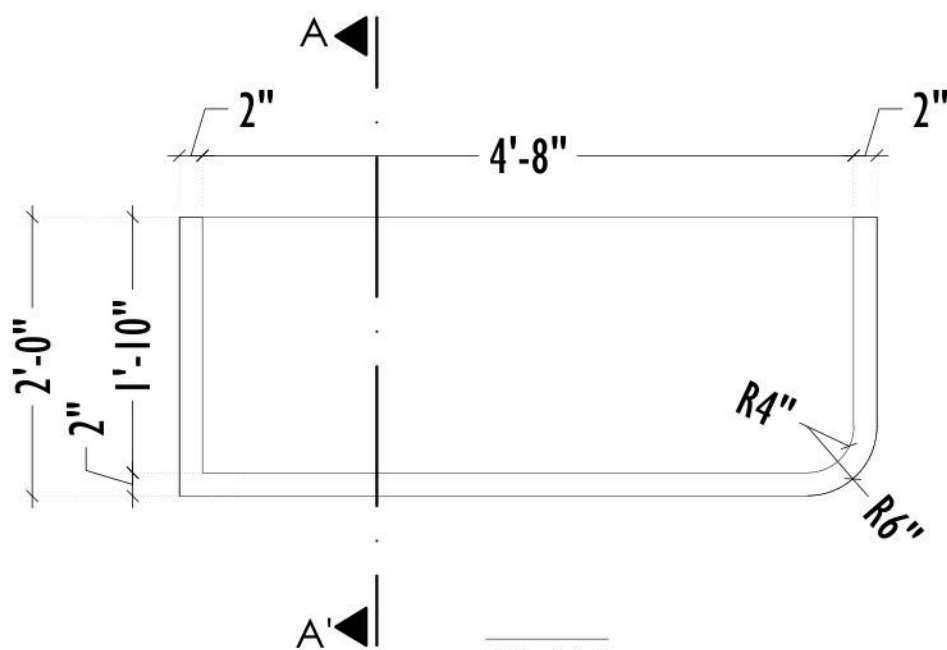

PLAN

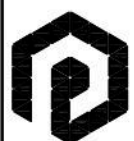

STUDIO PIRALI
135 D, Ground floor, Opposite
Guwahati Club
Guwahati 781003
Contact No:- 9560834775
studiopirali@gmail.com

NOTES :

1. THIS DRAWING IS THE PROPERTY OF STUDIO PIRALI & SHALL NOT BE USED IN ANY WAY WITHOUT THEIR WRITTEN PERMISSION.
2. ALL DIMENSION ARE IN MM. UNLESS OTHERWISE MENTIONED.
3. WRITTEN DIMENSION ARE TO BE FOLLOWED. DRAWING NOT TO BE SCALED.
4. STRUCTURAL DWG TO BE REFERRED ALONG WITH ARCHITECTURAL DWG.
5. CONTRACTOR SHOULD VERIFY THE DRAWINGS IN FIELD BEFORE COMMENCEMENT OF THE WORK.
6. IN CASE OF ANY DISCREPANCY CONTACT STUDIO PIRALI PRIOR TO EXECUTION.

PROJECT TITLE
HOME EXPERIA
Begusarai, Bihar

DRAWING TITLE :-
RECEPTION
COUNTER

DRAWING ISSUED:

☒	FOR APPROVAL
☐	GOOD FOR CONSTRUCTION
☐	FOR INFORMATION ONLY

DATE 27.07.2024
DEALT BY
CHECKED BY Dipankar
SCALE N.T.S

REVISONS	NO.	DATE	REMARKS	DWG. NO -F-109