



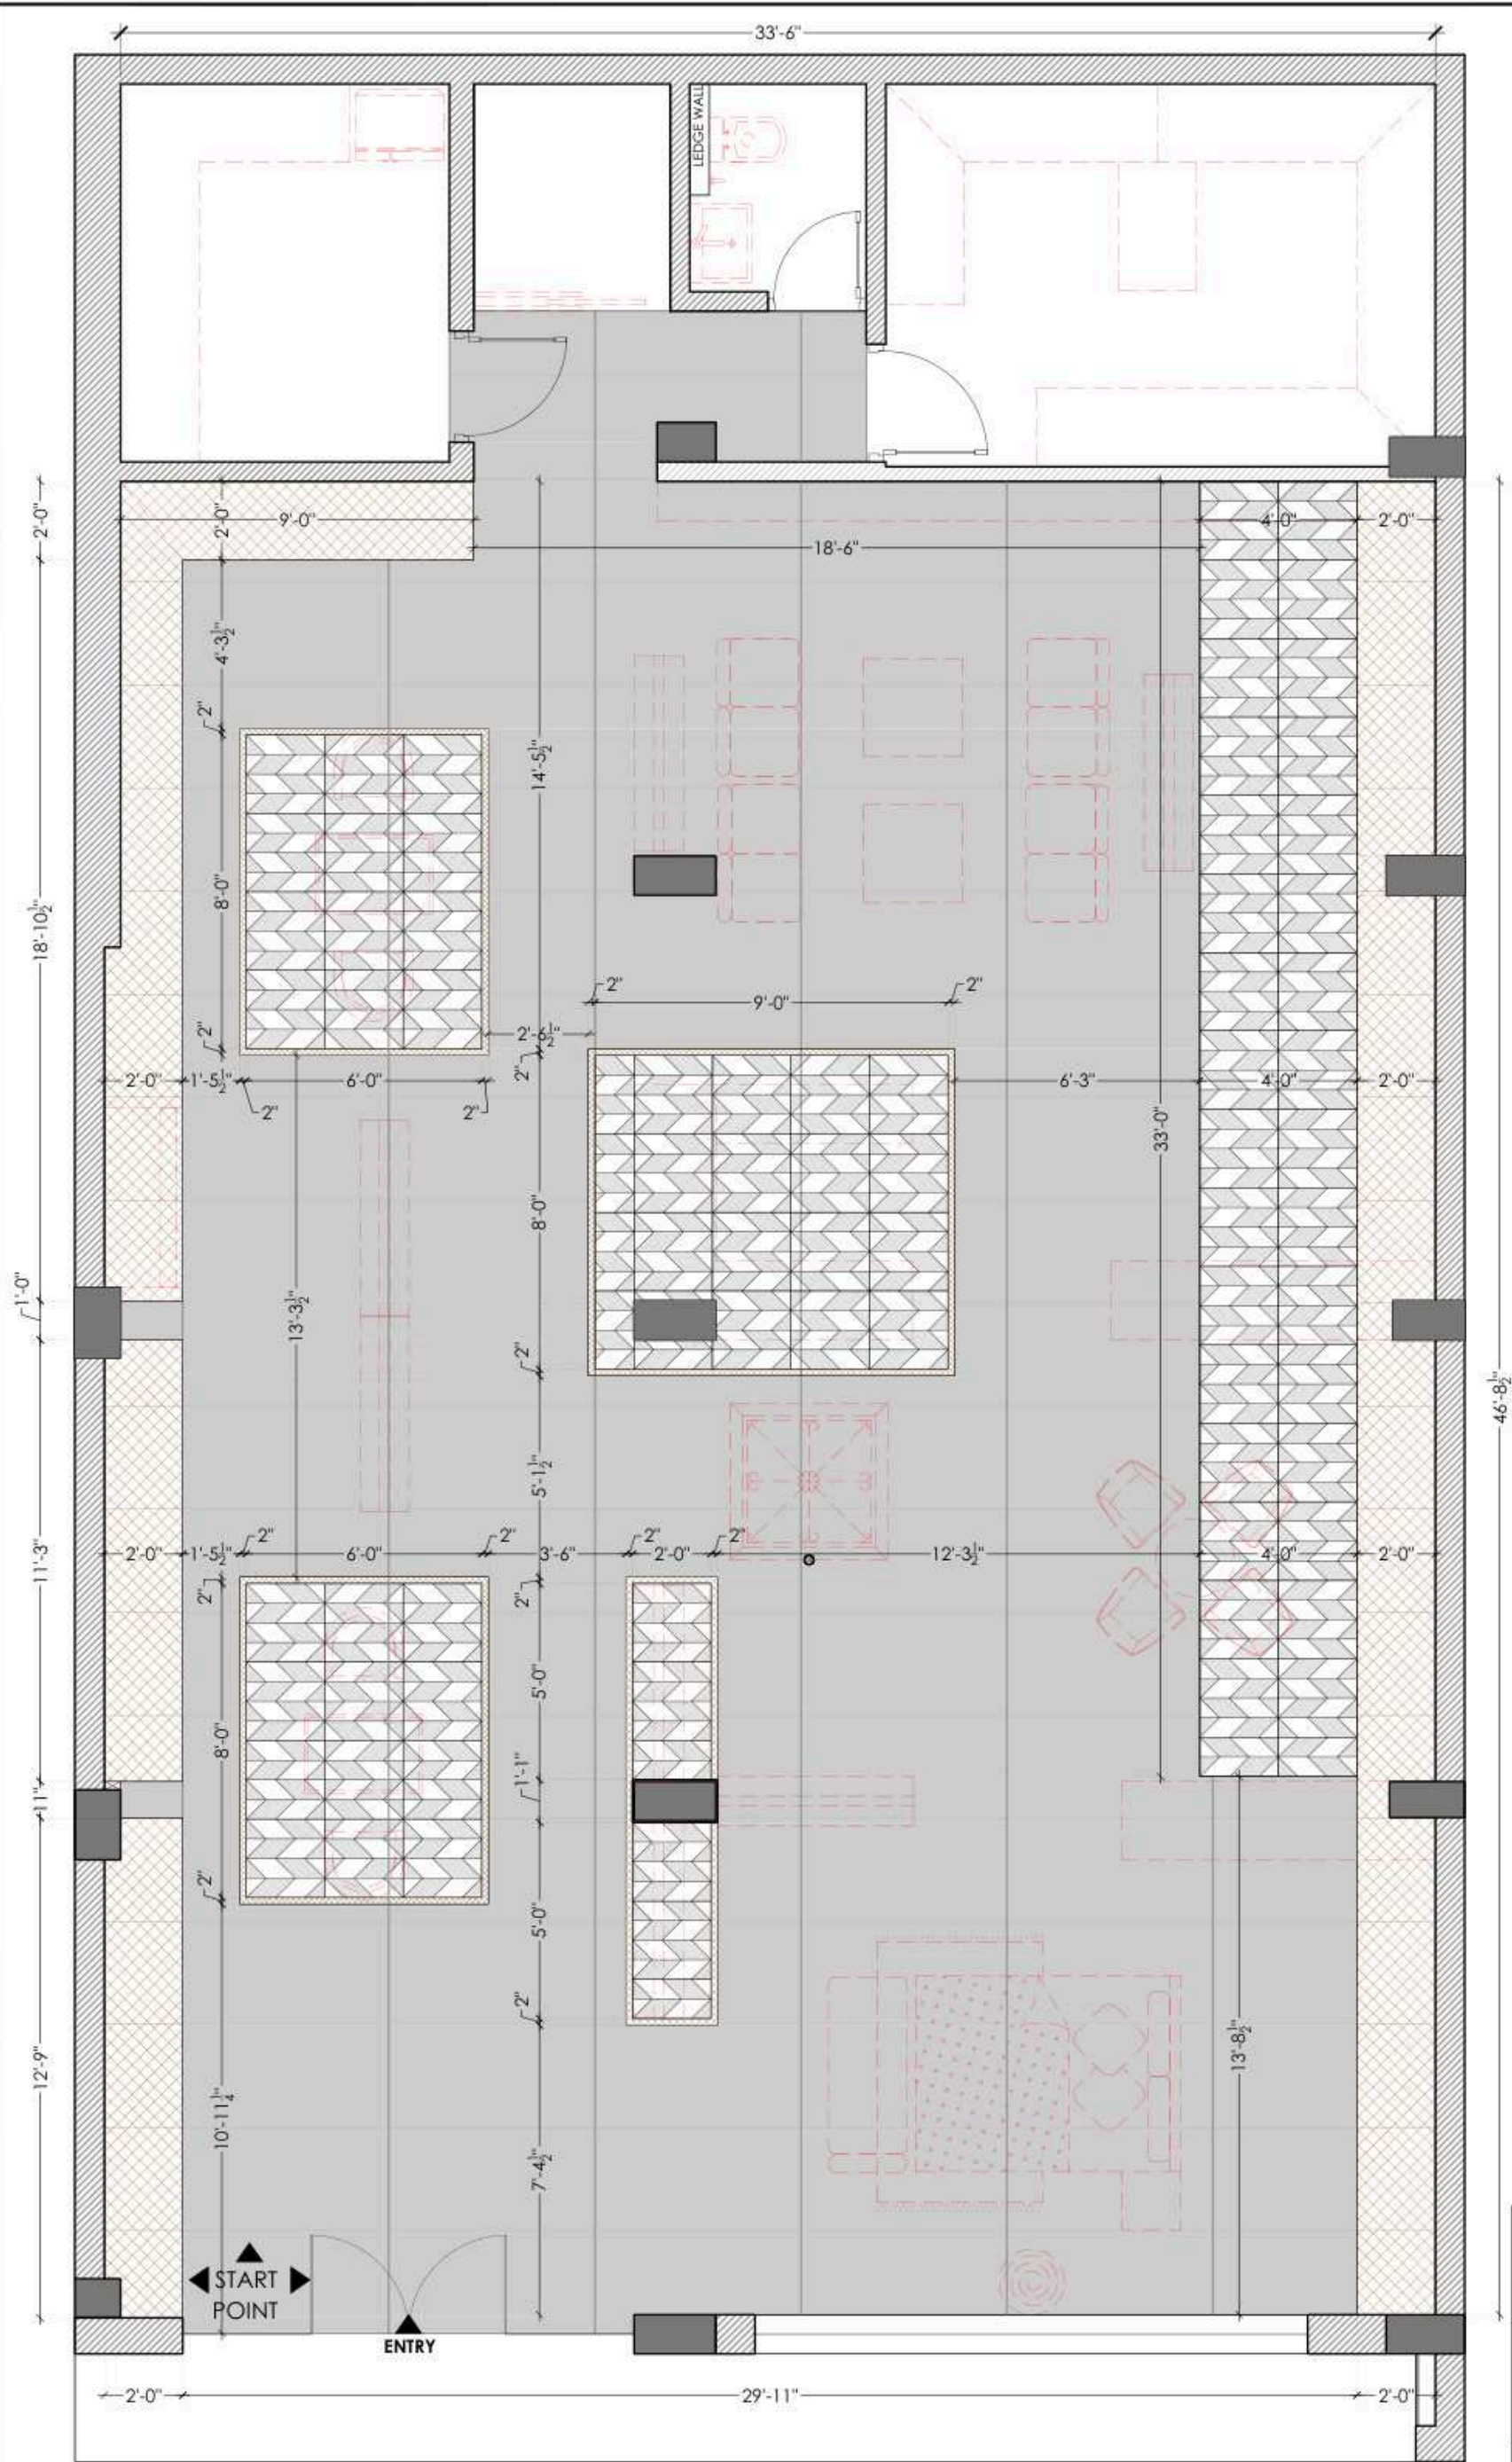

FLOORING LEGEND

	BAYONA SAND GLAZED VITRIFIED TILES COLLECTION- MAGNIFIED LT- Size800 X 1600 mm MAKE NITCO TILE	1095 SQ. FT.
	FLOORING AS PER APPROVAL	320 SQ. FT.
	COSENZA BRUNETTE GLAZED VITRIFIED TILES COLLECTION-MAGNIFIED LT-SIZE-800 X 1600 mm MAKE NITCO TILE	208.07 SQ. FT.

ARCHITECTS :		NOTES :	PROJECT TITLE	DRAWING TITLE :-	DRAWING ISSUED:		DATE	21.07.2024	REVISIONS	NO	DATE	REMARKS	DWG. NO - 01
	STUDIO PIRALI 135 D, Ground floor, Opposite Guwahati Club Guwahati 781003 Contact No:- 9560834775 studiopirali@gmail.com	1. THIS DRAWING IS THE PROPERTY OF STUDIO PIRALI & SHALL NOT BE USED IN ANY WAY WITHOUT THEIR WRITTEN PERMISSION. ALL DIMENSION ARE IN MM. UNLESS OTHERWISE MENTIONED, WRITTEN DIMENSION ARE TO BE FOLLOWED. DRAWING NOT TO BE SCALED. 2. STRUCTURAL DWG TO BE REFERRED ALONG WITH ARCHITECTURAL DWG. 3. CONTRACTOR SHOULD VERIFY THE DRAWINGS IN FIELD BEFORE COMMENCEMENT OF THE WORK. 4. IN CASE OF ANY DISCREPANCY CONTACT STUDIO PIRALI PRIOR TO EXECUTION.	HOME EXPERIA Begusarai, Bihar	FLOORING PLAN	☐	FOR APPROVAL	DEALT BY			01			
					☒	GOOD FOR CONSTRUCTION	CHECKED BY	<i>Syankar</i>		02			
					☐	FOR INFORMATION ONLY	SCALE	N.T.S		03			

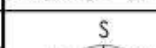